
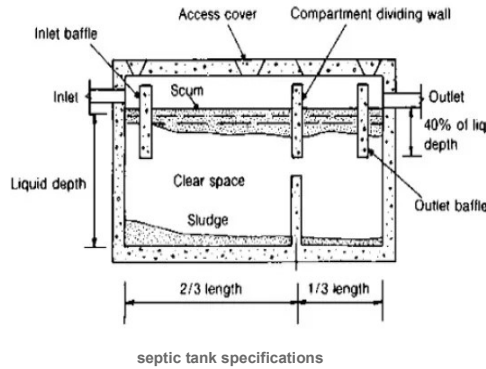
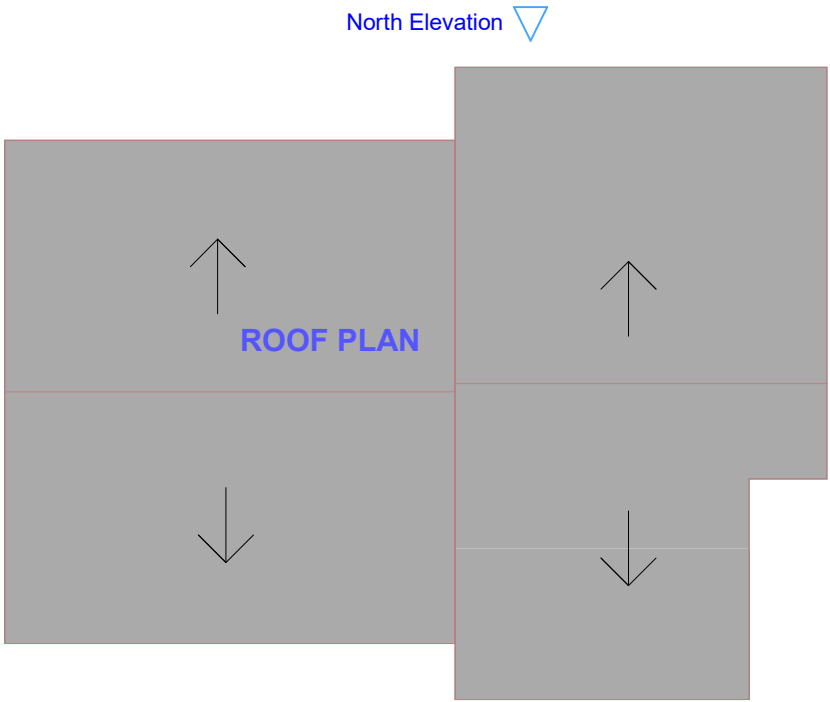


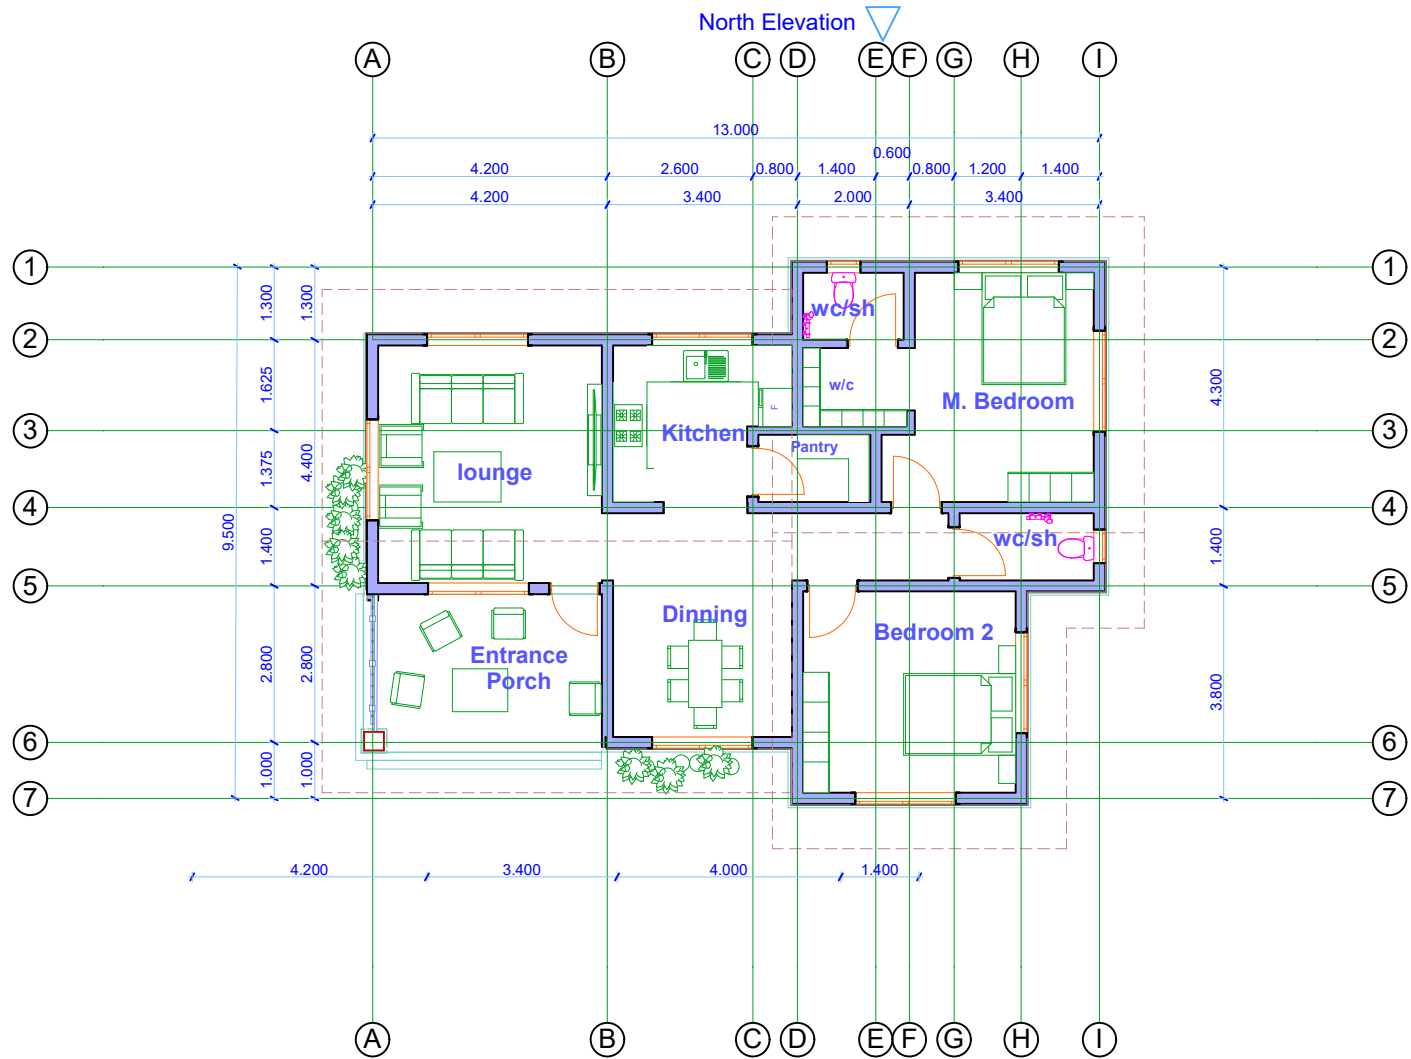

THE DRAWINGS
COPYRIGHT OF THE AUTHOR
IT IS ILLEGAL TO USE THE DRAWING FOR PURPOSES
OF CONSTRUCTION OR TO REPRODUCE IT IN PART OR
IN WHOLE WITHOUT THE AUTHOR'S PRIOR CONSENT

NOTES

1. All measurements are shown in millimeters. Drawings not to be scaled. Only figured dimensions to be used.
2. The contractor must check and verify all dimensions on site before commencement of work. Any discrepancies must be notified immediately to the architect and clarified.

CONSTRUCTION

3. Damp proof course must be provided under all external walls at grade. DPC to be min. 150mm above GL.
4. All slab at grade to be poured on 1000 Gauge polythene on 50mm stone dust blinding on hardcore.
5. All soil under slab and around external foundations to be poisoned for anti-termite control.
6. window sills must be finished before internal plastering.
7. All RC work to structural engineer's details.
8. Depth of foundation to be determined on site to S.E approval
9. All walls shall be 150mm thick unless otherwise shown
10. All walls shall be reinforced with approved hoop iron at every alternate course.

MECHANICAL

11. Drain pipes passed beneath buildings and driveways to be encased in 150mm concrete surround.
12. All mechanical work must be coordinated with electrical work. Any conflicts must be clarified before works begin.
13. Minimum slopes in drain pipes shall be 1%.
14. All testing of pipes must be completed before plastering.

NOTE

This drawing is an architectural concept/preliminary design prepared for visualization and planning purposes. Prior to implementation, the design should be reviewed, refined where necessary, and finalized by a BORAGS-registered architect together with a licensed structural engineer to ensure compliance with applicable regulations and project requirements.

Revision History

RevID	ChID	Change Name	Date

Company Title

PROPOSED 2 BEDROOM HOUSE
PROJECT

CLIENT:

DESIGNED BY:

SIGN

CHECKED BY:

SIGN


SHEET TITLE
FLOOR PLAN,
ELEVATION, SECTION

SCALE

1:100


SHEET NO

A.01

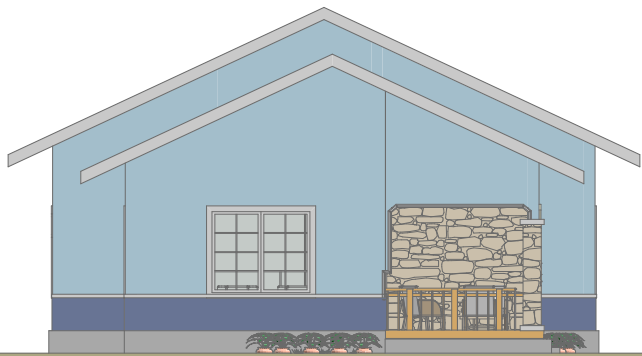


West Elevation

1:100

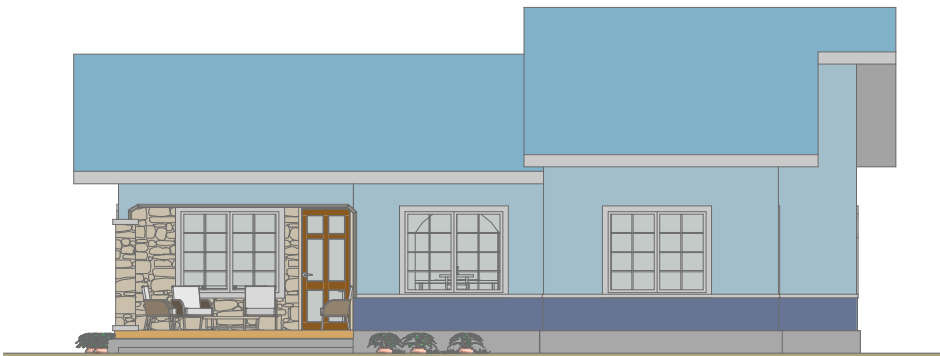


South Elevation

1:100

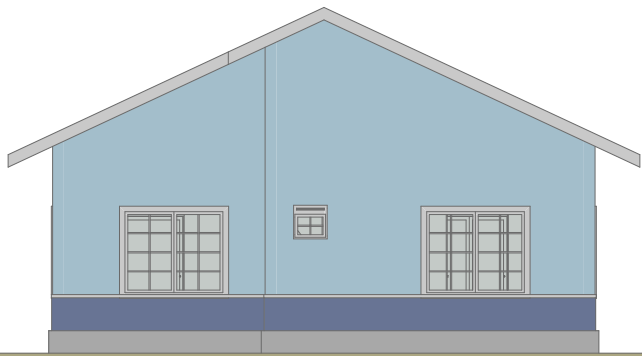




East Elevation

1:100

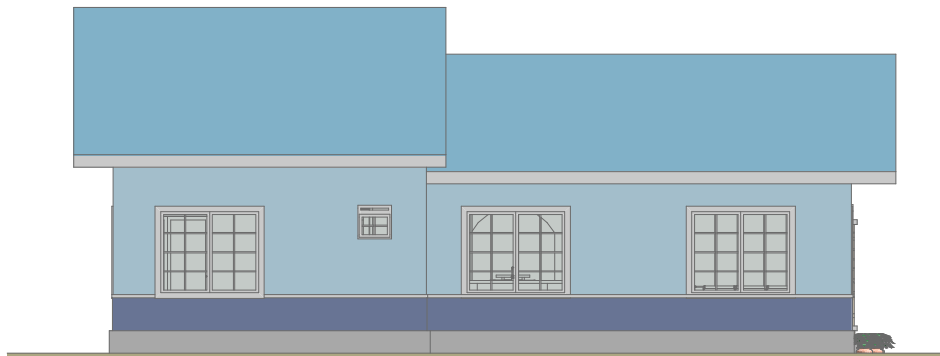

North Elevation

1:100

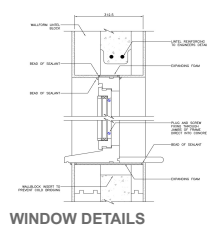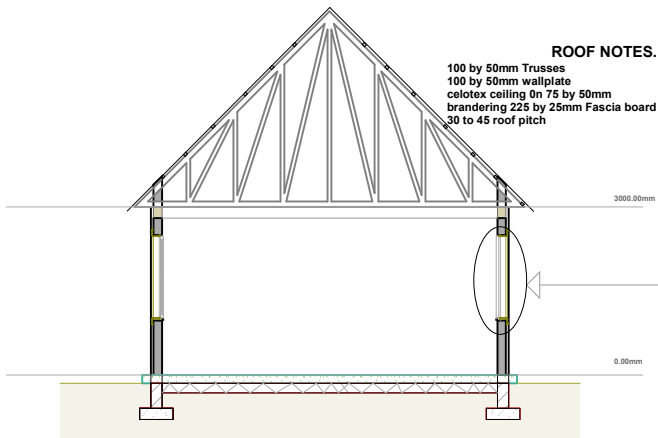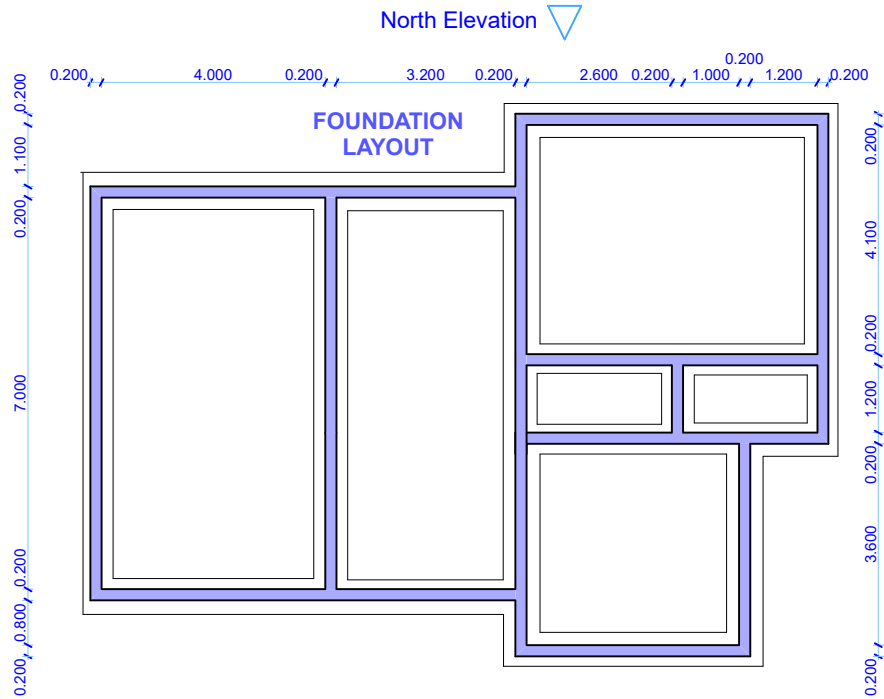

FOUNDATION NOTES.

Foundation on 150mm conc. slab on 1000G polythene
sheet DPM on 50mm murrum blinding on 300mm H/C fill.
600 by 200mm conc. in strip.