
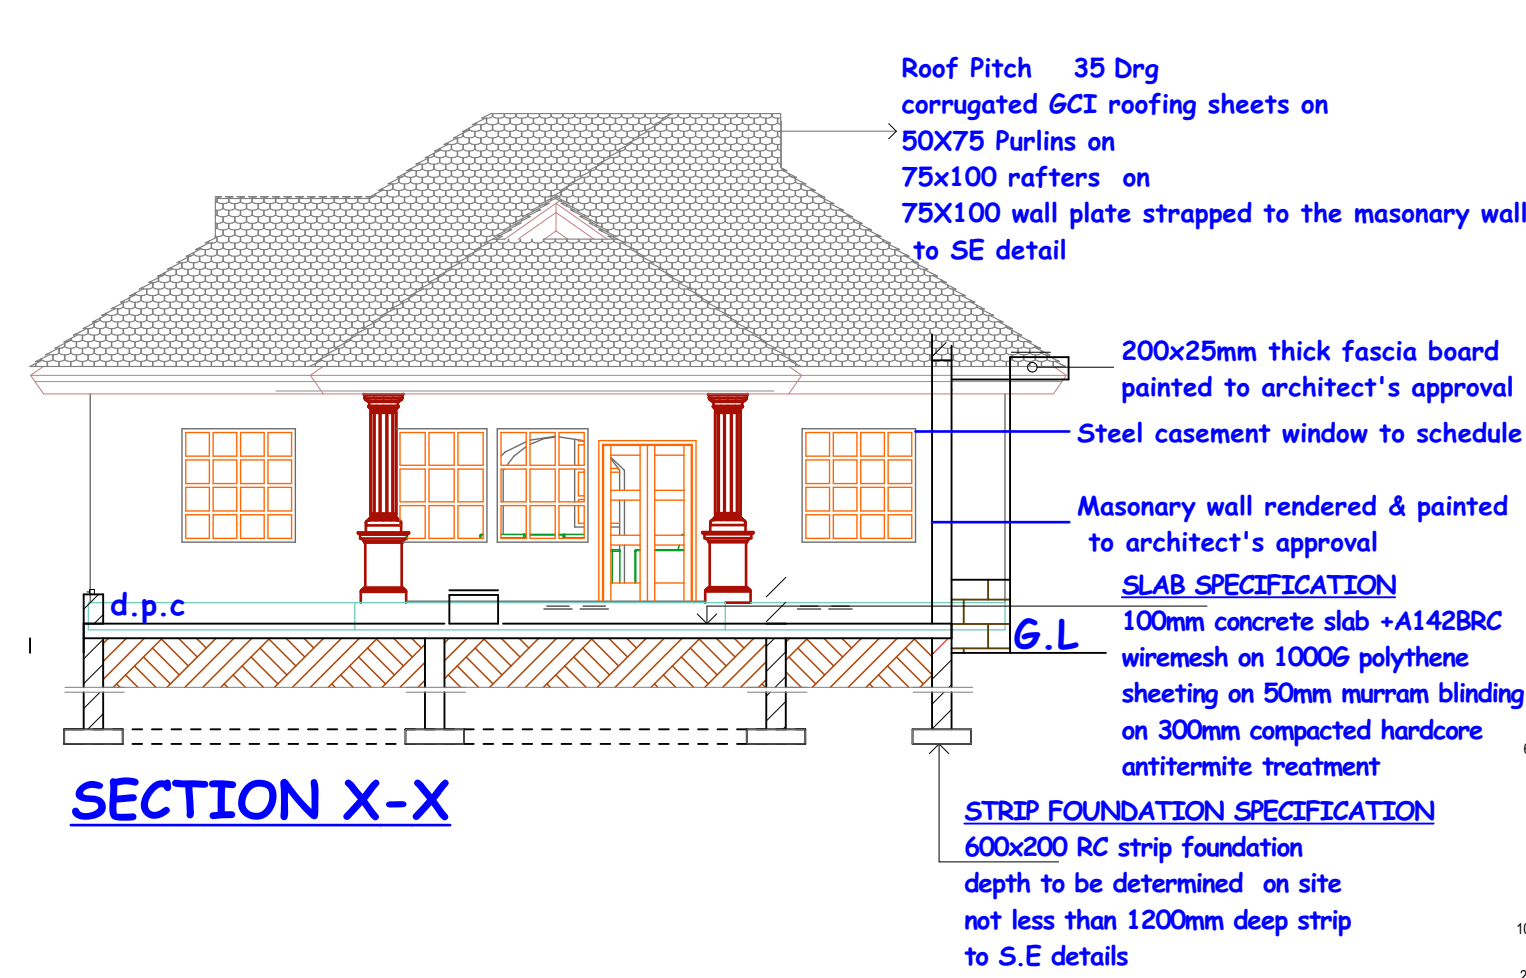


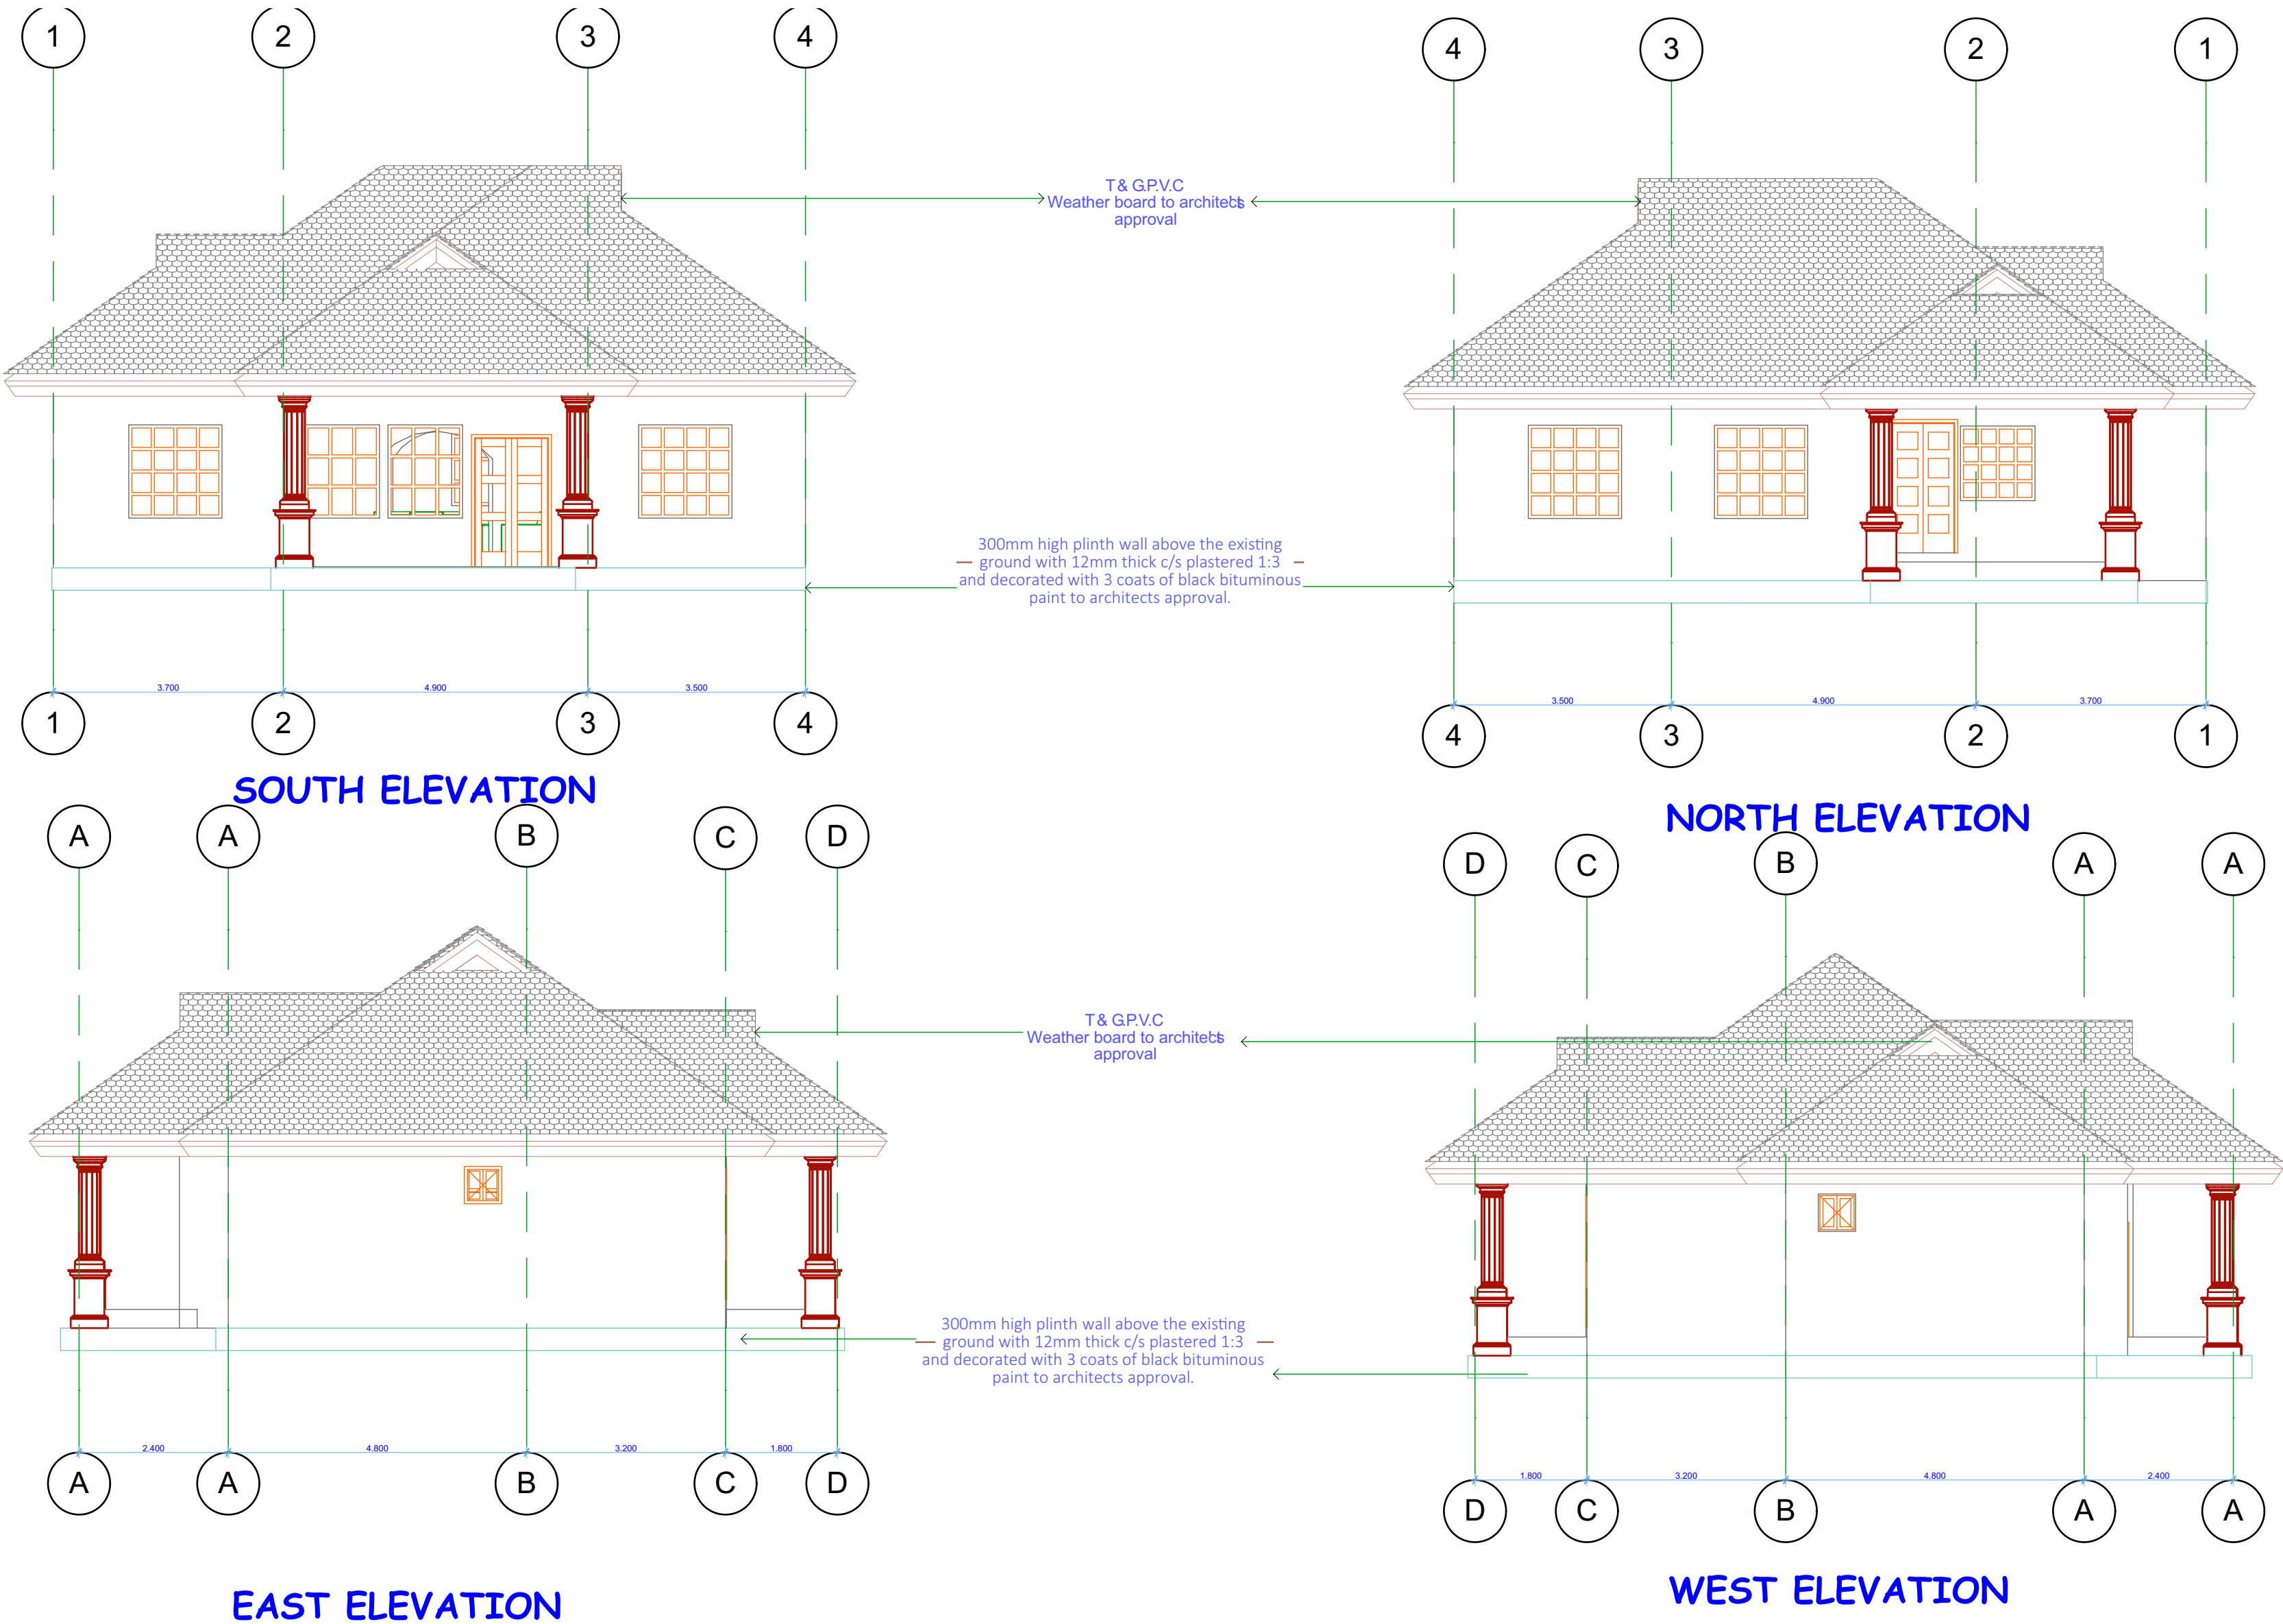

DOOR AND WINDOW SCHEDULE

WINDOW WIDTH	HEIGHT	DETAILS	DOOR	WIDTH	HEIGHT	DETAILS
W1	5 by4	STEELCASEMENT	D1	1200	2100	STEELCASEMENT
W2	4 by4	STEELCASEMENT	D2	1200	2100	STEELCASEMENT
W3	4 by4	STEELCASEMENT	D3	900	2100	TIMBER
W4	4 by4	STEELCASEMENT	D4	900	2100	TIMBER
W5	5 by4	STEELCASEMENT	D5	900	2100	TIMBER
W6	4 by4	STEELCASEMENT	D6	900	2100	TIMBER
W7	2 by2	STEELCASEMENT	D7	900	2100	TIMBER
W8	2 by2	STEELCASEMENT	D8	900	2100	TIMBER
W9	2 by2	STEELCASEMENT	D9	900	2100	TIMBER
W10	2 by2	STEELCASEMENT	D10	900	2100	TIMBER
		DECORATIVE WINDOW 2NO	D11	2500	2100	GARAGE DOOR
			GRILLS	6.6Metres	1M	rear porch
				7.7Metres		entry porch

- GENERAL NOTES**
- All dimensions to be checked on site and if necessary confirm with the architect
 - All Reinforced concrete work will be in accordance with structural drawings
 - All walls below 200mm to be reinforced with hoop iron at every alternate course
 - DPC to be 3ply Bituminous felt to be provided under all walls
 - Permanent vents to be provided as shown on plan
 - Where drainage is shown under driveways and slabs To be encased 160mm thick concrete surround
 - All ICs within building area drive way and parking to have heavy Duty double seal air tight covers and walls to be 200mm
 - All Basins, baths, and Sinks to be fitted with antivacuum traps
 - All fire doors to be one & half hour fire resistant doors
 - All plumbing & drainage works to comply with M.Q.H. regulations
 - All S&W.V.P.to be approved 100mm dia.Pvc pipes encased in chicken mesh and conc surround to be plastered & painted or finished in ceramic tiles
 - Termitor or Equal & approved anti termite treatment & 1000 gauge polythene sheeting cover to be provided under all ground floor concrete slab on compacted hardcore to approval
 - All softwood to be cell cured & approved to be painted or polished
 - Plinth level to be a minimum 300mm from proposed parking level or existing ground level
- RAIN WATER DISPOSAL**
- All pitched roofs to have 100x150mm 22gauge G.I. box gutters and 75mm dia p.v.c down pipes in ducts and other appropriate accessories all to be painted. R.W.D.P. to dispose at ground level into 300x300x300mm conc. sump & cement gullies to detail
 - All concrete used in floors, columns and beams to be strictly 1:2:4 mix
 - Mortars for bonding blocks to be strictly 1:4 mix
 - All marble and granite tiles to be protected from red soil marks by totally covering with polythene sheeting & to be finished smooth with machine polish filling all gaps
- 3.All Terrazzo to be finished smooth with terrazzo polish to Architects approval
- 4.All ceramic floors to be protected from soil marks

REVISIONS

No.	Date	Revision/Issue

Project; Title PROPOSED CONSTRUCTION OF A 3 BEDROOM HOUSE

Client

Client Signature.....

Drawing Title




PLANS SECTION ELEVATIONS
AND SITE PLAN

SCALE : 1:100

DATE :

DRAWN BY :

Signature

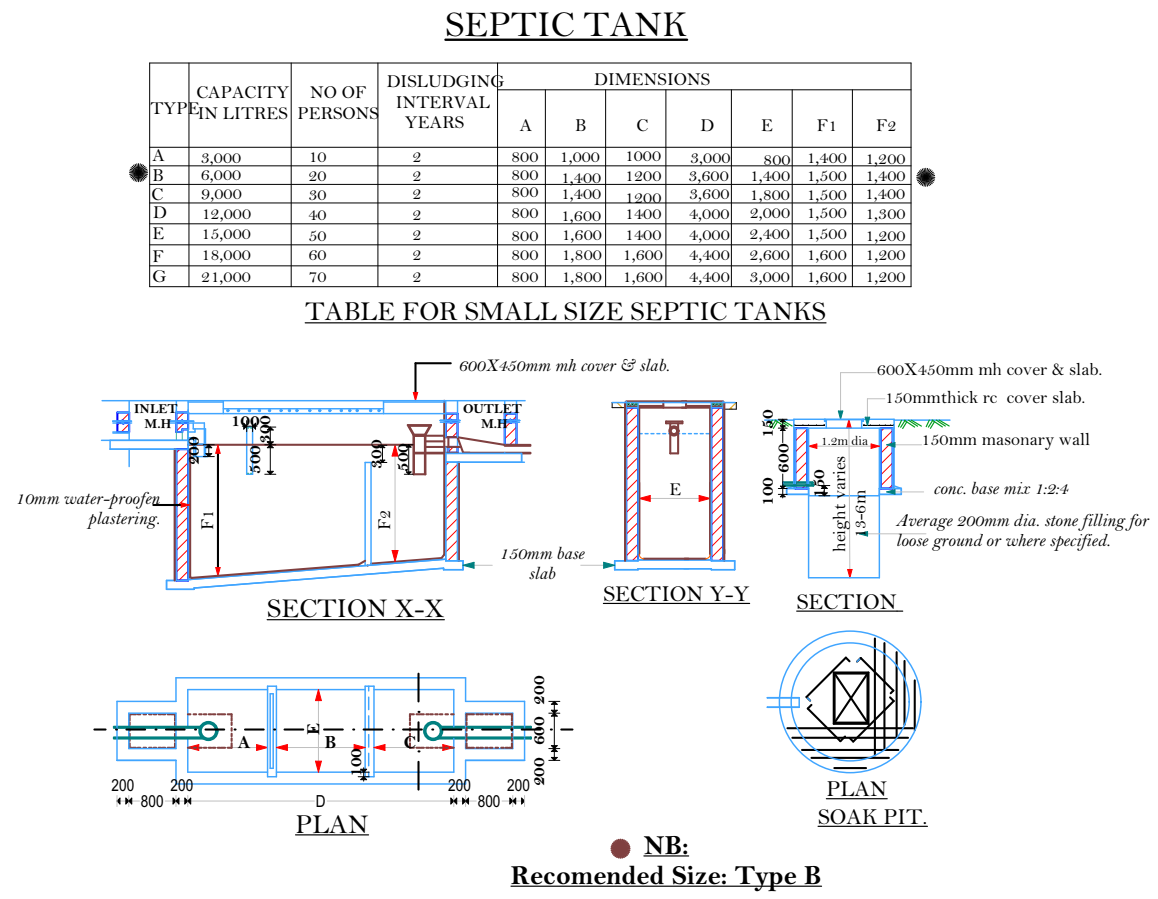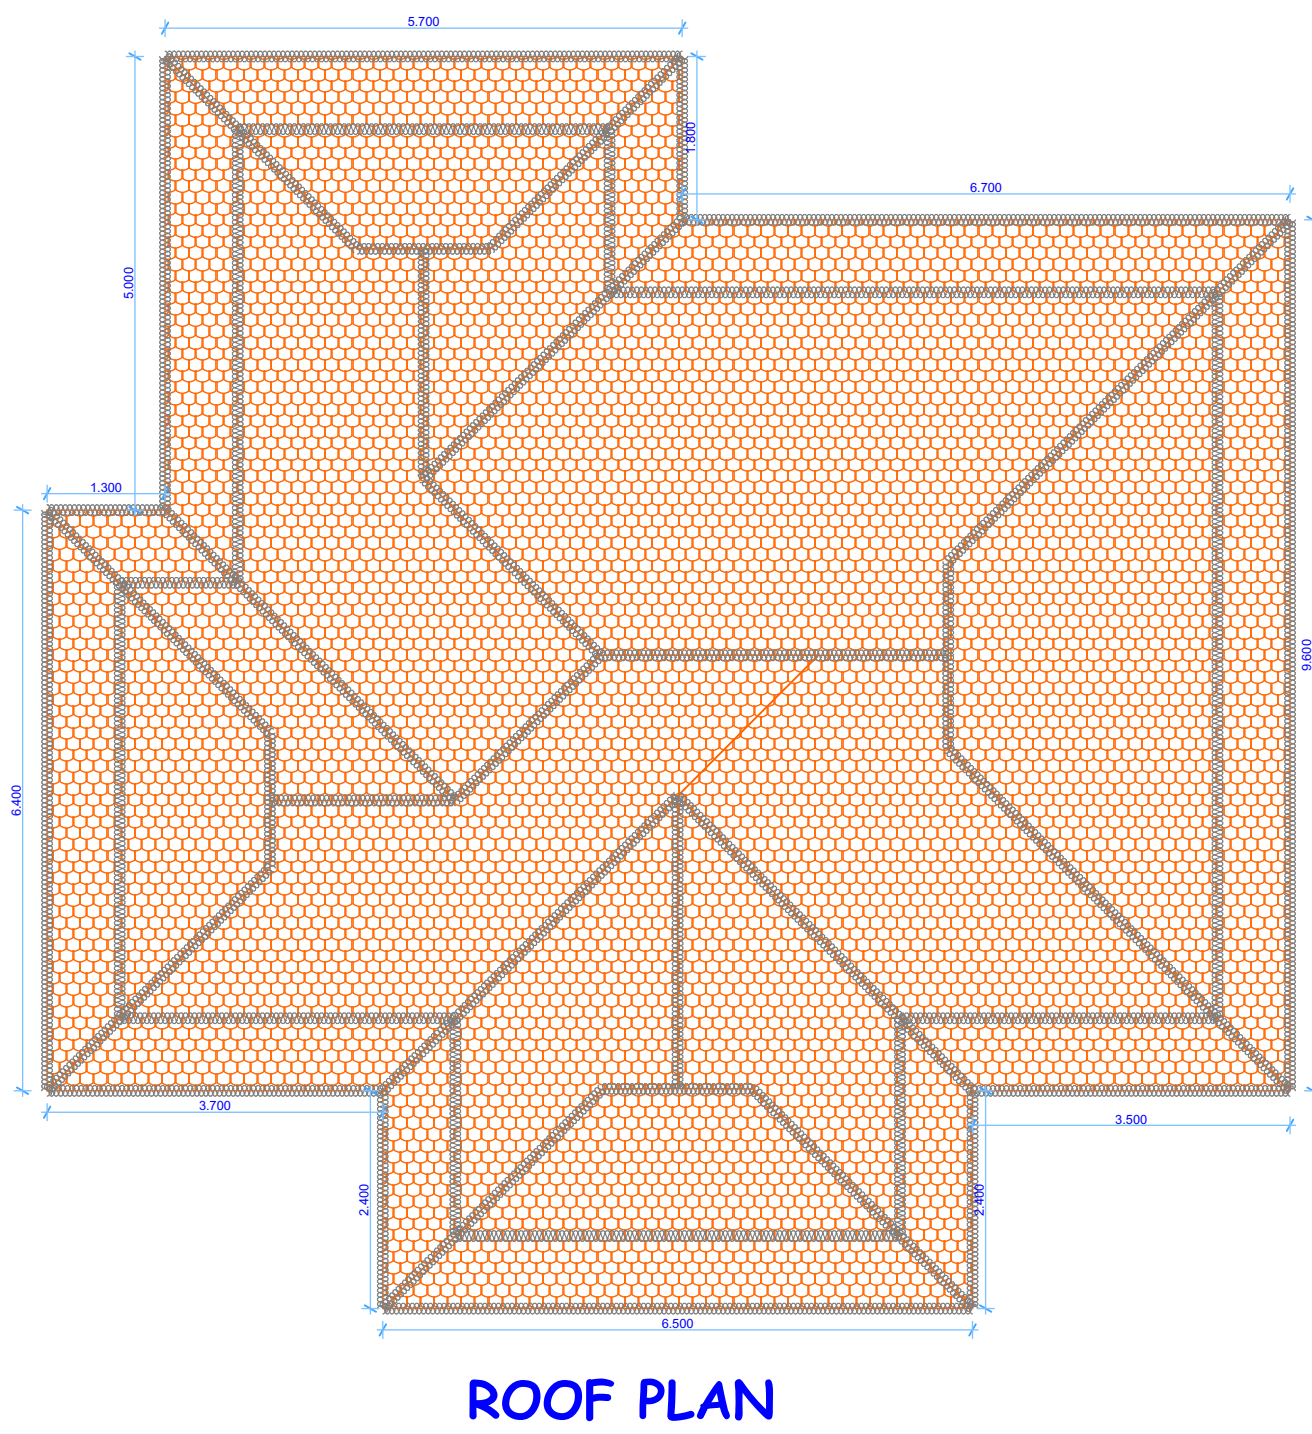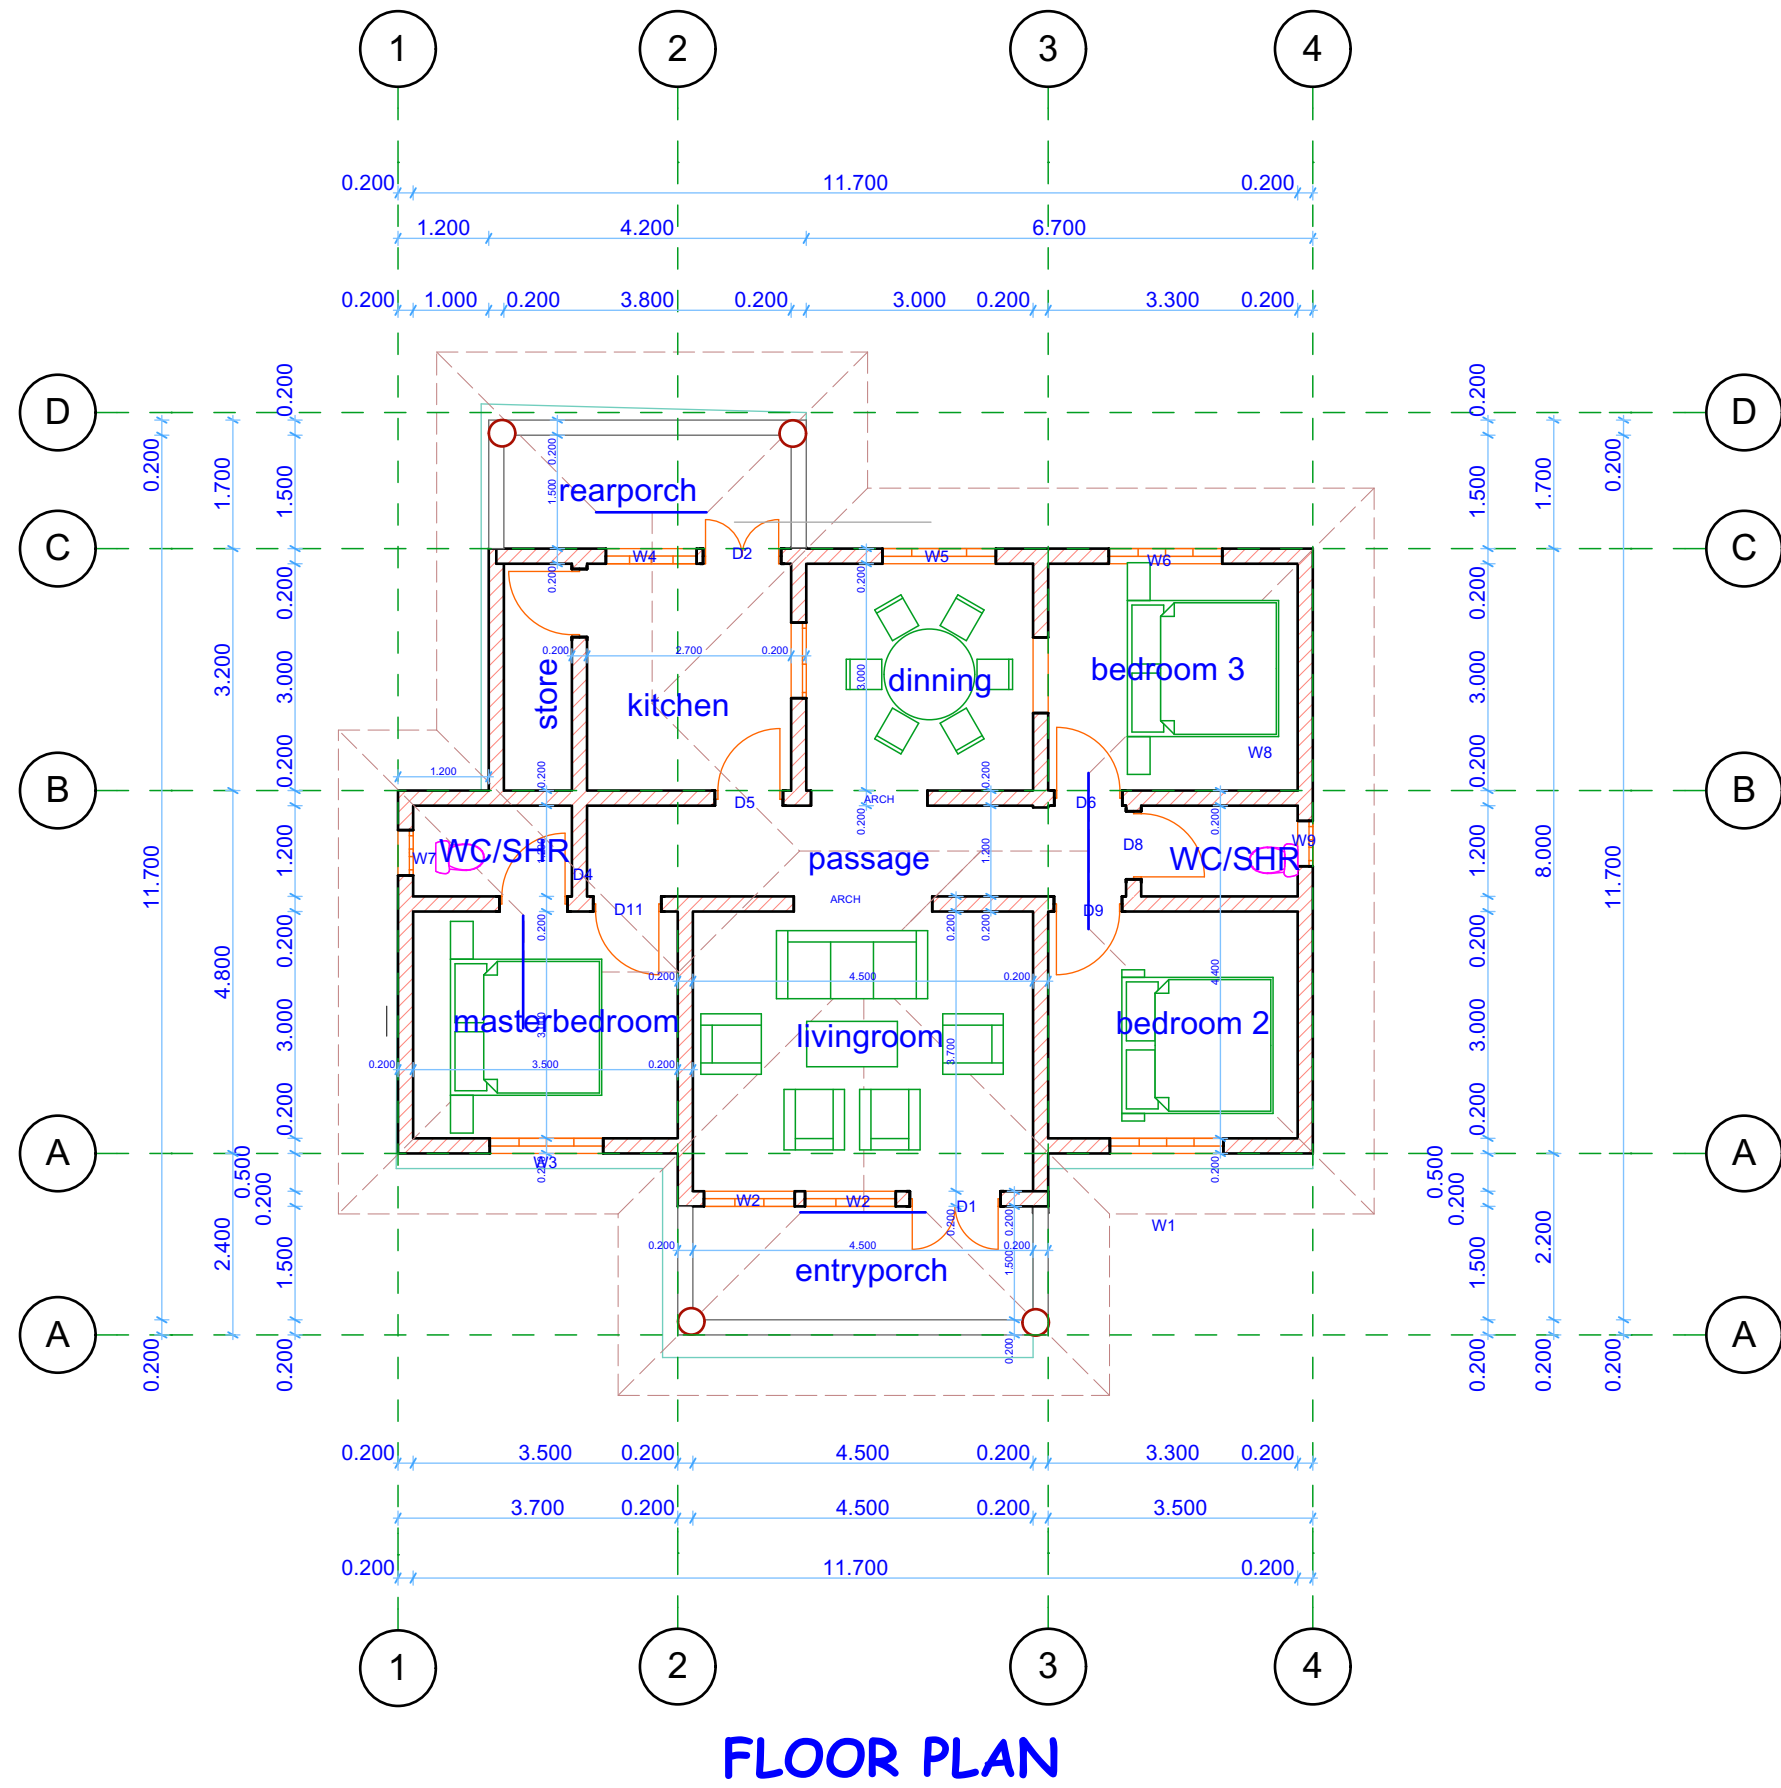

SITE PLAN