




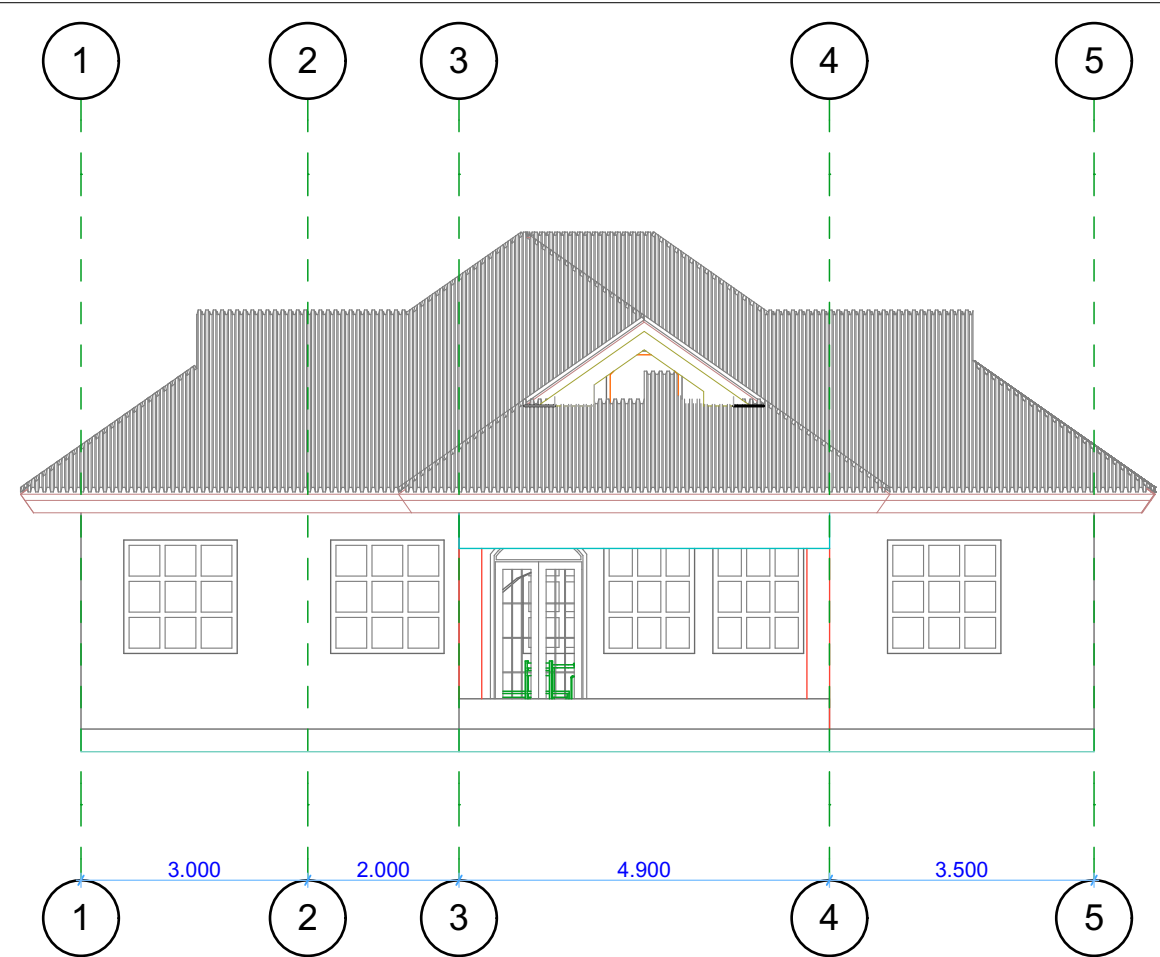


FRONT ELEVATION

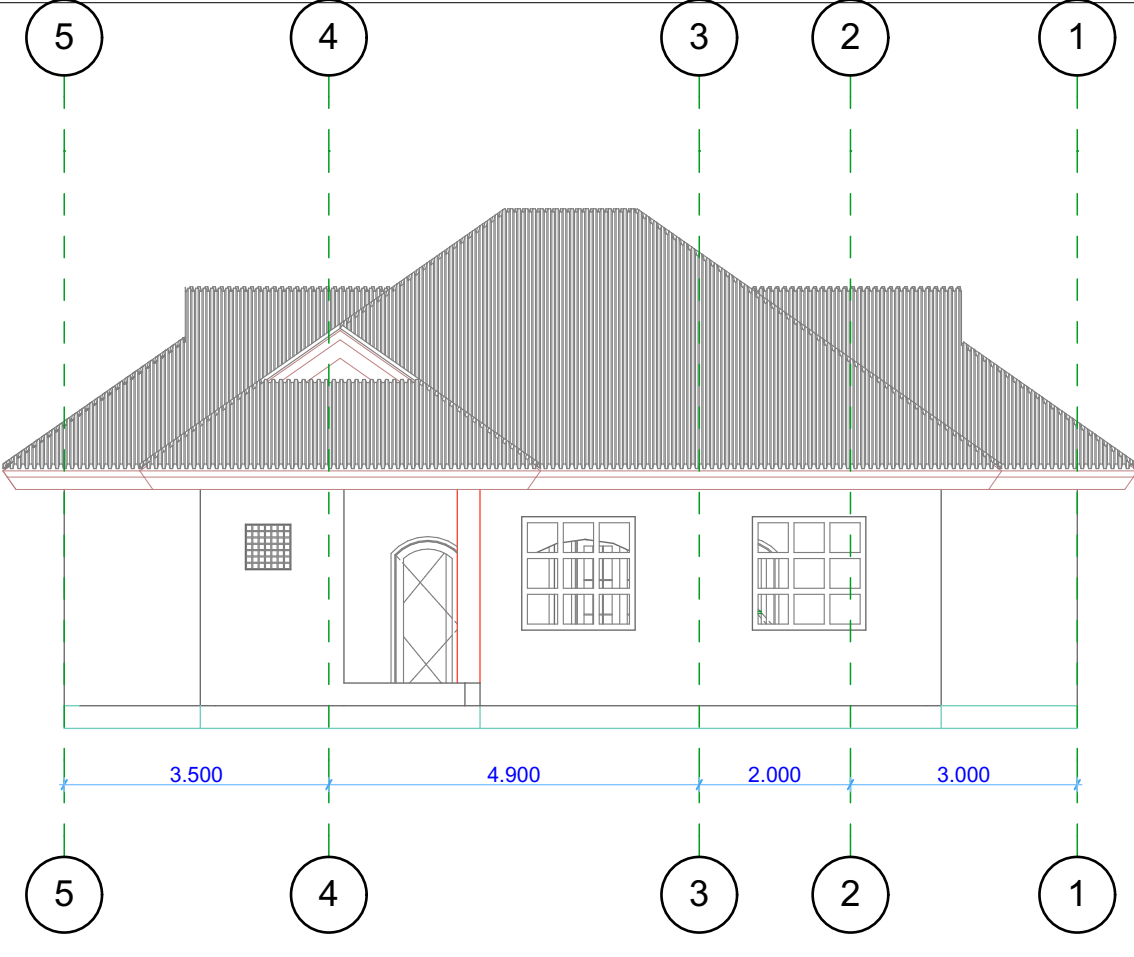


REAR ELEVATION

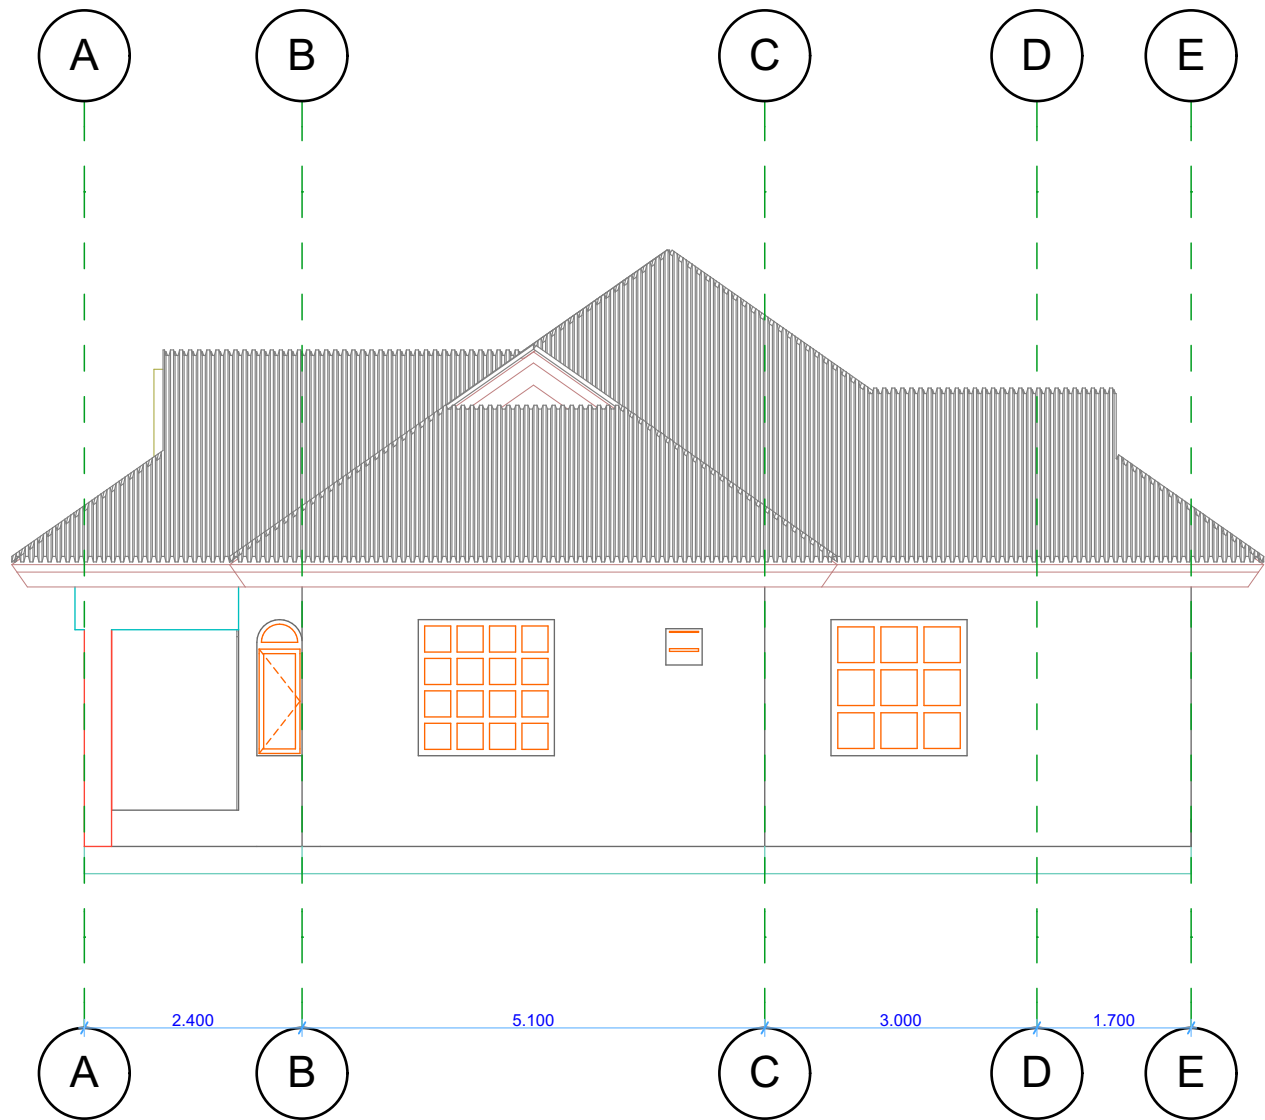


SIDE ELEVATION

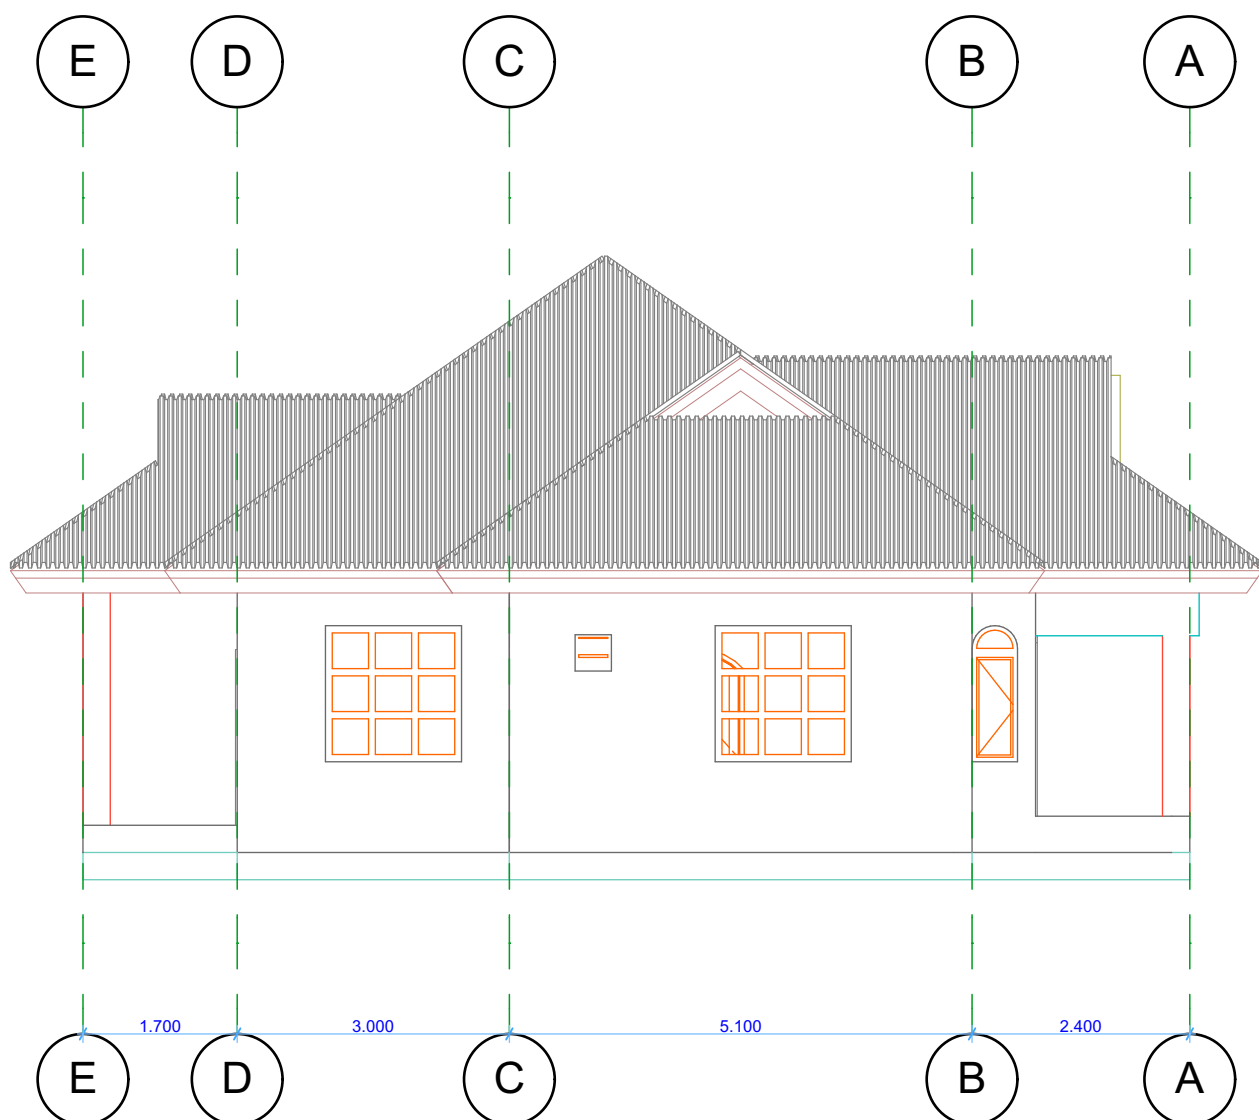


SIDE ELEVATION 2

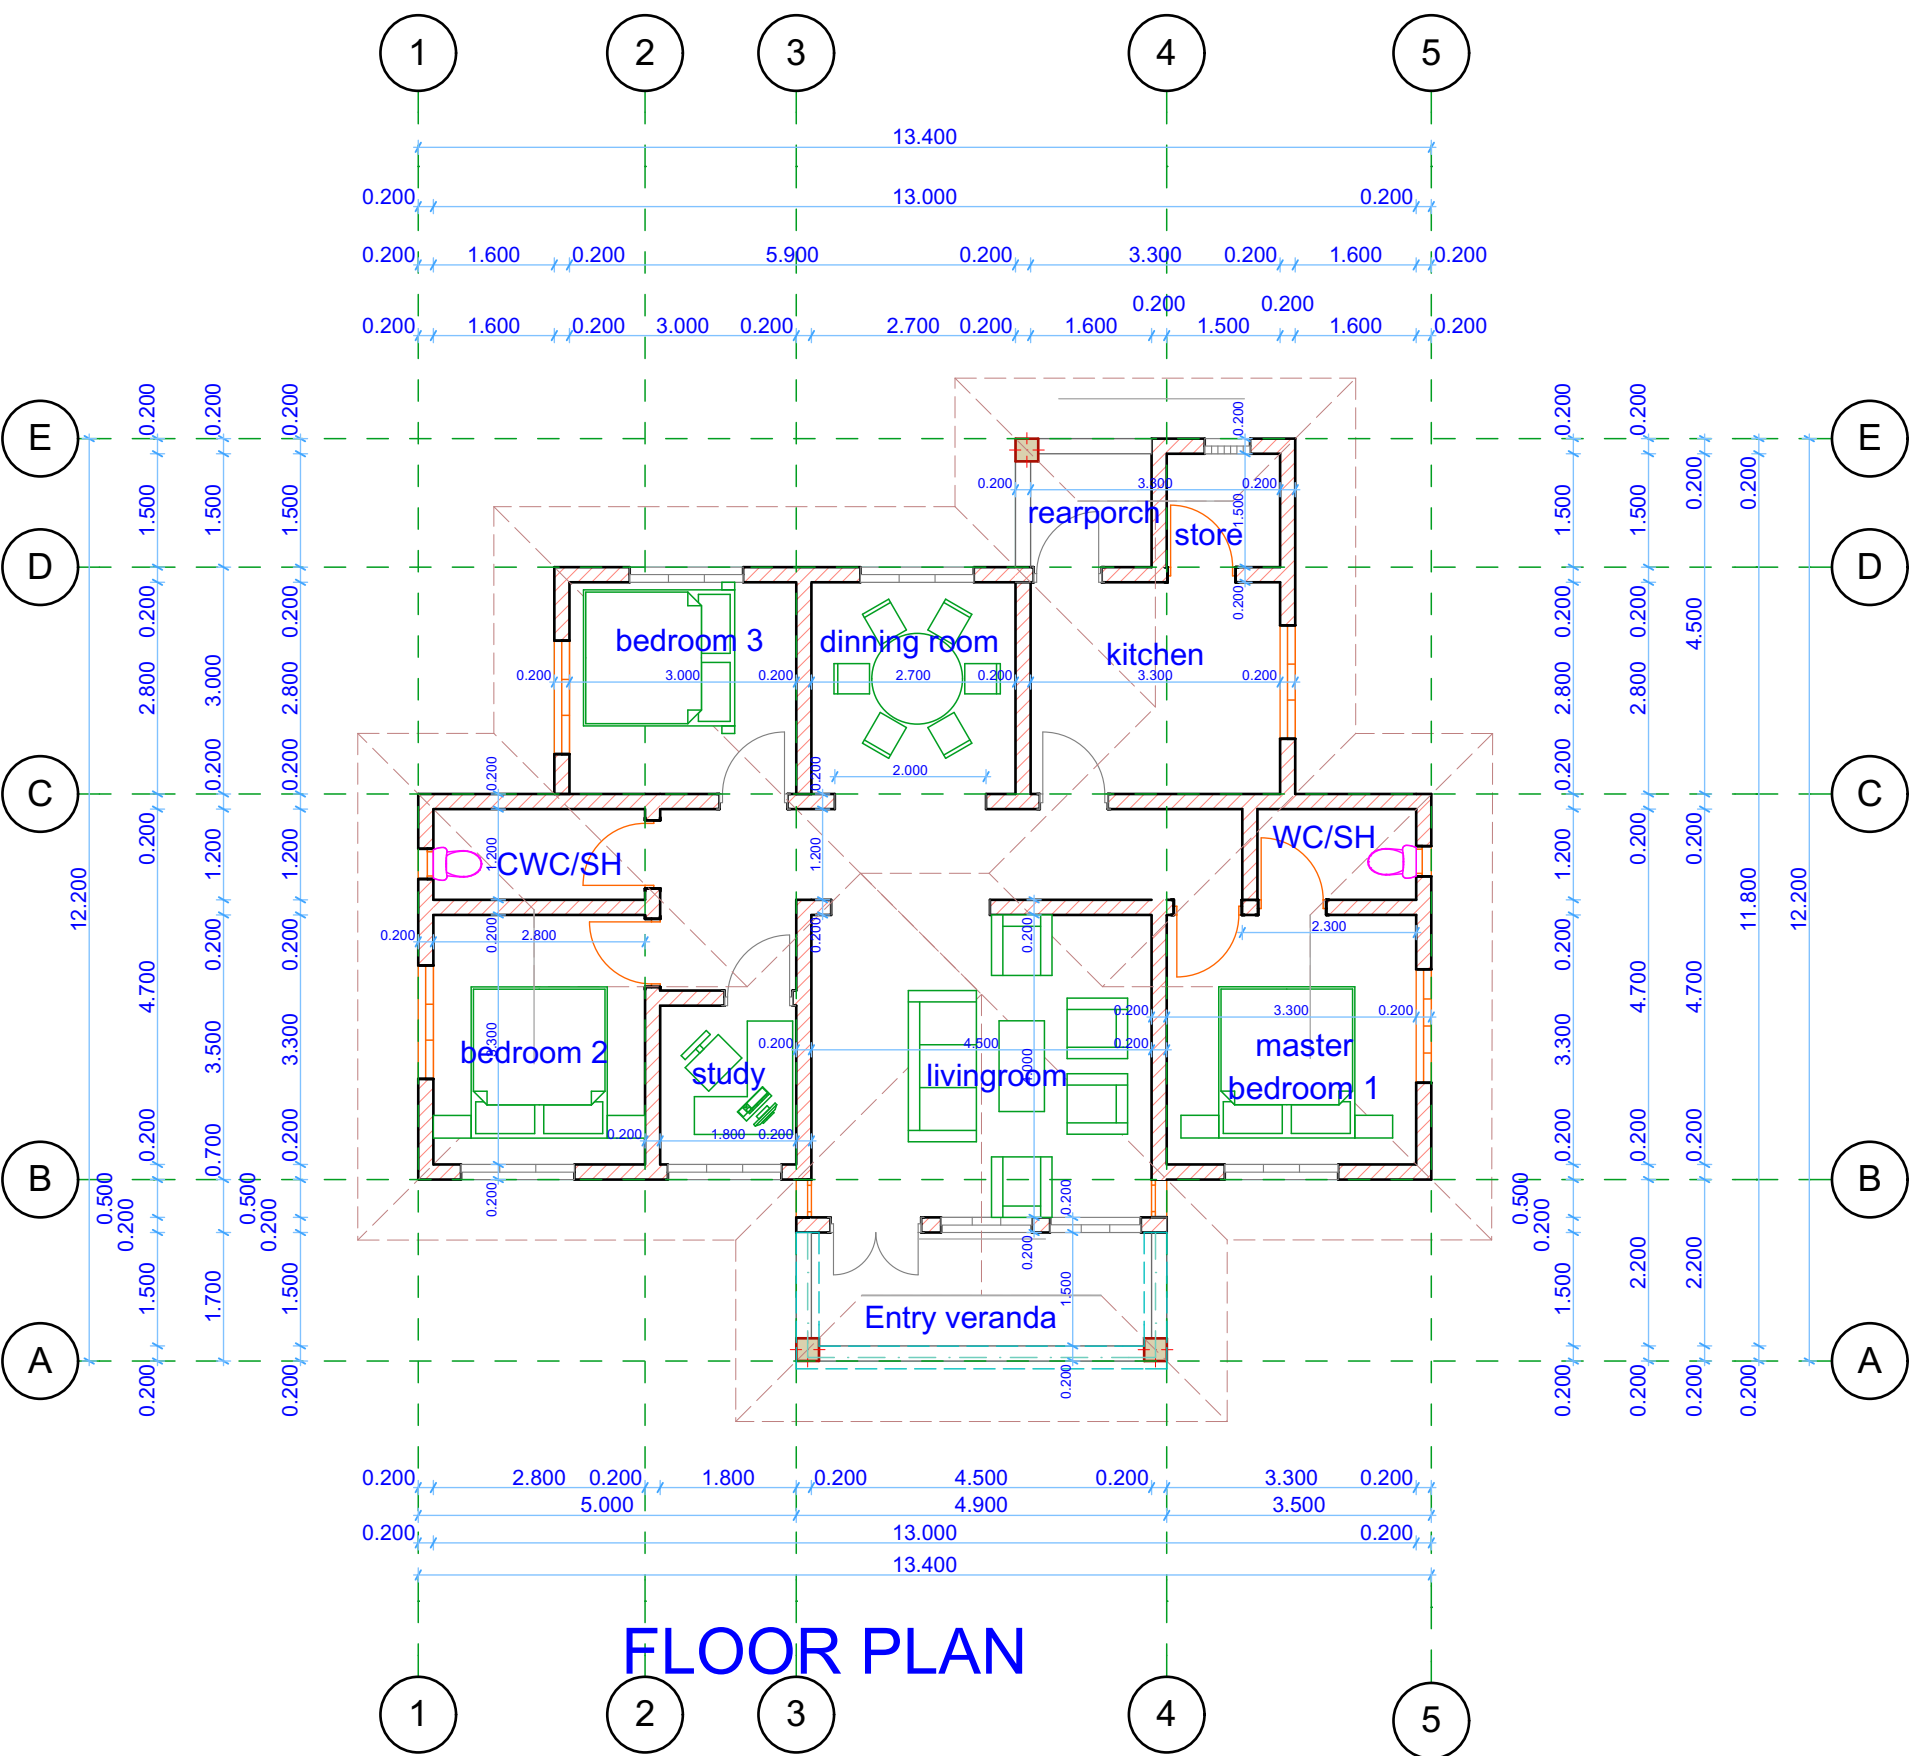

FLOOR PLAN

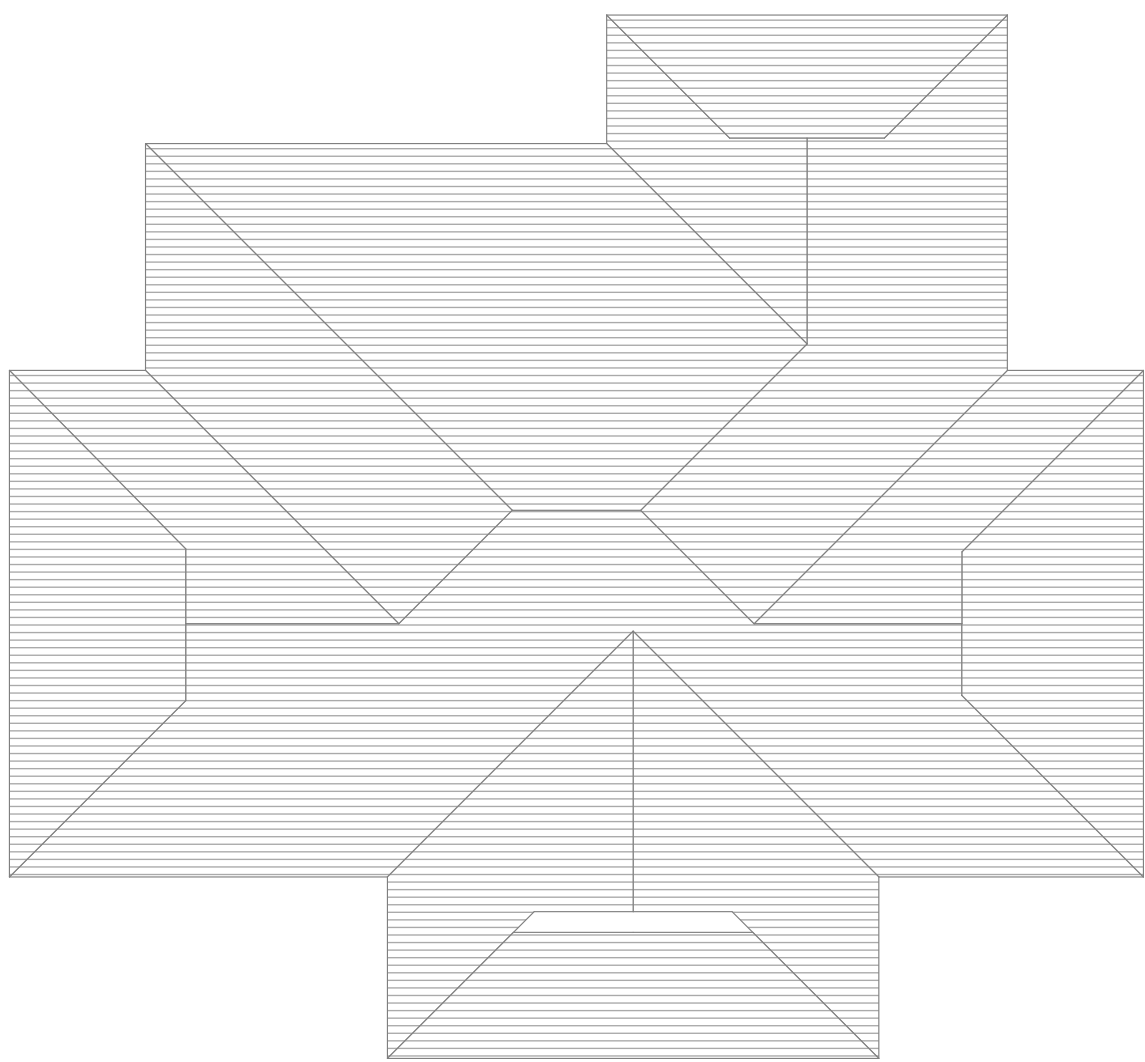

ROOF PLAN

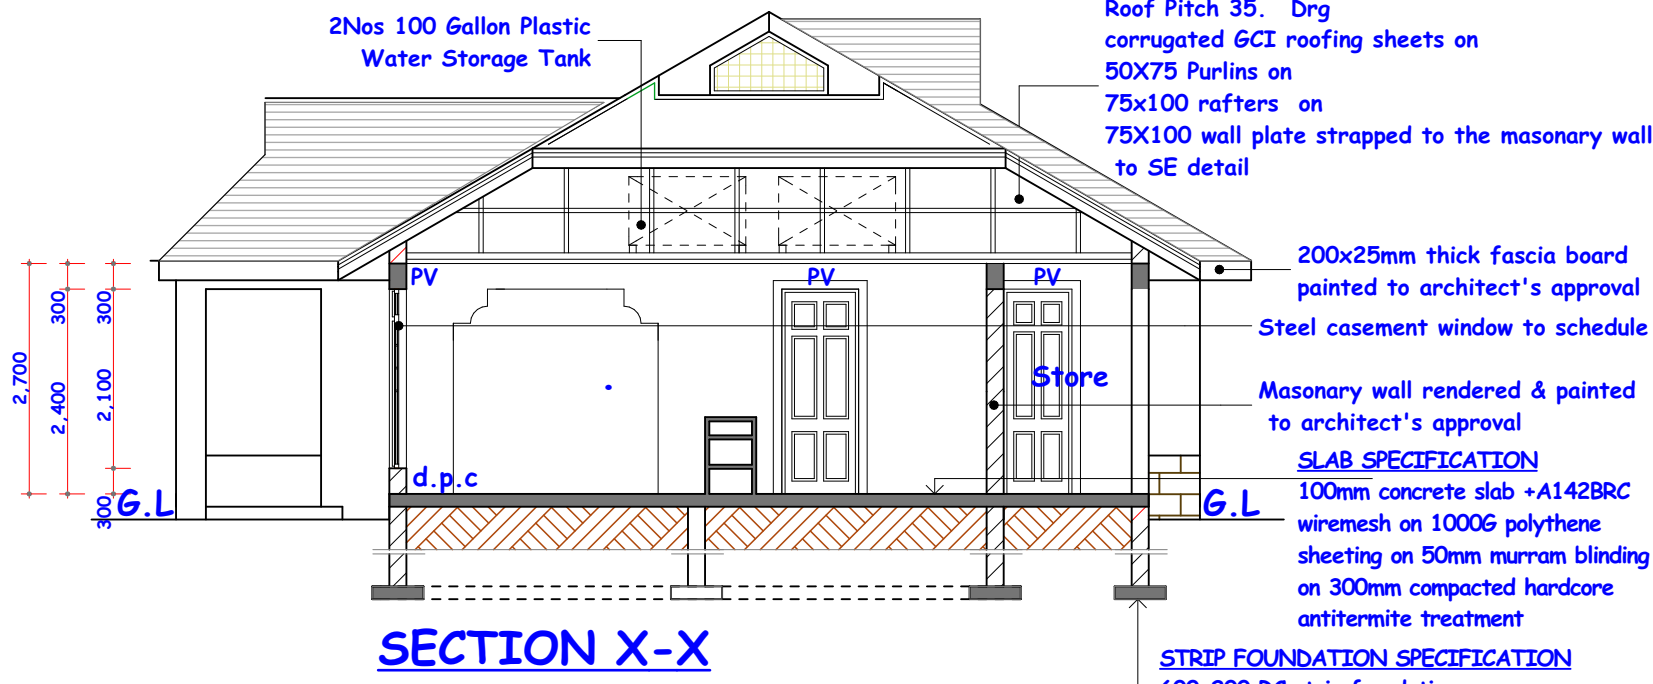


SECTION X-X

DOOR AND WINDOW SCHEDULE

| WINDOW | WIDTH | HEIGHT | DETAILS       |
|--------|-------|--------|---------------|
| W1     | 1500  | 1500   | STEELCASEMENT |
| W2     | 1500  | 1500   | STEELCASEMENT |
| W3     | 1500  | 1500   | STEELCASEMENT |
| W4     | 1500  | 1500   | STEELCASEMENT |
| W5     | 1500  | 1500   | STEELCASEMENT |
| W6     | 1500  | 1500   | STEELCASEMENT |
| W7     | 1500  | 1500   | STEELCASEMENT |
| W8     | 1500  | 1500   | STEELCASEMENT |
| W9     | 1500  | 1500   | STEELCASEMENT |
| W10    | 1500  | 1500   | STEELCASEMENT |
| W11    | 600   | 600    | STEELCASEMENT |
| W12    | 600   | 600    | STEELCASEMENT |
| W13    | 600   | 600    | STEELCASEMENT |
| W14    | 1500  | 1200   | STEELCASEMENT |

| DOOR | WIDTH | HEIGHT | DETAILS       |
|------|-------|--------|---------------|
| D1   | 1500  | 2100   | STEELCASEMENT |
| D2   | 900   | 2100   | TIMBER        |
| D3   | 900   | 2100   | TIMBER        |
| D4   | 900   | 2100   | TIMBER        |
| D5   | 900   | 2100   | TIMBER        |
| D6   | 1200  | 2100   | STEELCASEMENT |
| D7   | 900   | 2100   | TIMBER        |
| D8   | 900   | 2100   | TIMBER        |
| D9   | 900   | 2100   | TIMBER        |
| D10  | 900   | 2100   | TIMBER        |

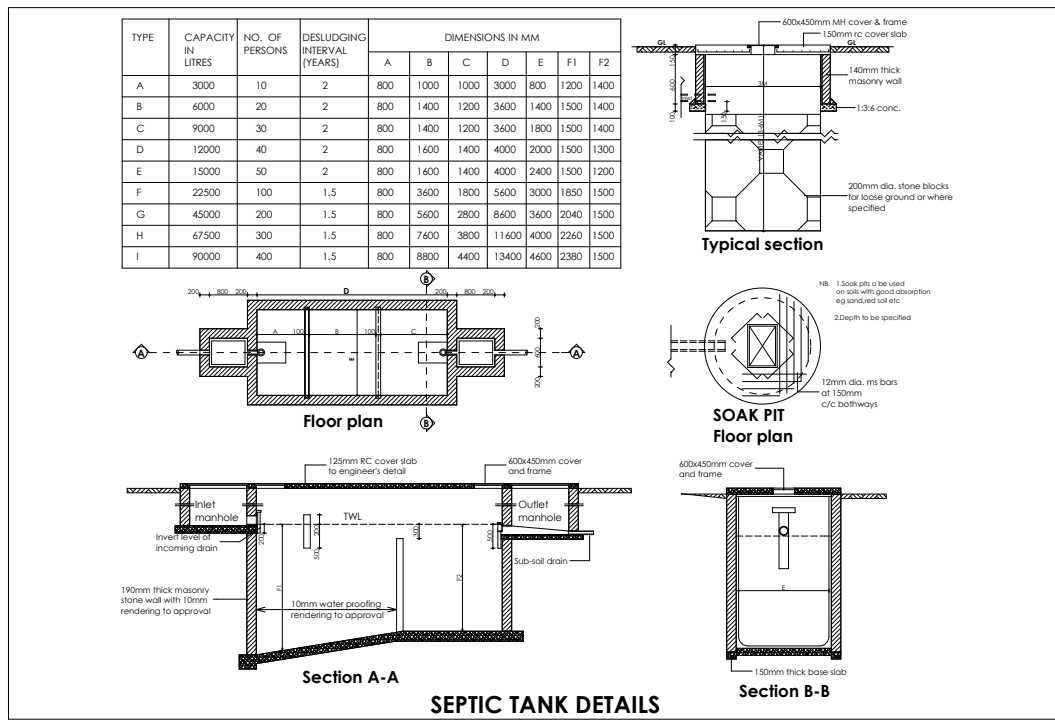

SEPTIC TANK DETAILS

GENERAL NOTES

- All dimensions to be checked on site and if necessary confirm with the architect
- All Reinforced concrete work will be in accordance with structural drawings
- All walls below 200mm to be reinforced with hoop iron at every alternate course
- DPC to be 3ply Bituminous felt to be provided under all walls.
- Permanent vents to be provided as shown on plan
- Where drainage is shown under driveways and slabs To be encased in 150mmthick concrete surround.
- All ICs within building area, drive way and parking to have heavy Duty, double seal air tight covers and walls to be 200mm
- All Basins, baths, and Sinks to be fitted with antivacuum traps
- All fire doors to be one & half hour fire resistant doors
- All plumbing & drainage works to comply with M.O.H. regulations
- All S&W.V.P to be approved 100mm dia.Pvc pipes encased in chicken mesh and conc surround to be plastered & painted or finished in ceramic tiles
- Terimidor or Equal & approved anti termite treatment & 1000 gauge polythene sheeting cover to be provided under all ground floor concrete slab on compacted hardcore to approval

RAIN WATER DISPOSAL

- All pitched roofs to have 100x150mm 22gauge G.I. box gutters and 75mm dia p.v.c down pipes in ducts and other appropriate accessories all to be painted. R.W.D.P. to dispose at ground level into 300x300x300mm conc. sump & cement gullies to detail

- All concrete used in floors,columns and beams to be strictly1:2:4 mix

- Mortars for bonding blocks to be strictly 1:4 mix
- All marble and granite tiles tobe protected from red soil marks by totally covering with polythene sheeting & to befinished smooth with machine polish filling all gaps

- All Terrazzo to be finished smooth with terrazzo polish to Architects approval

- All ceramic floors to be protected from soil marks

REVISIONS

| No. | Date | Revision/Issue |
|-----|------|----------------|
|     |      |                |
|     |      |                |
|     |      |                |
|     |      |                |

Job Title:-

PROPOSED RESIDENTIAL DEVELOPMENT

ON PLOT No

Client:-

Client Signature.....

Drawing Title:-

PLANS,SECTION,ELEVATIONS AND SITE PLAN

Scale 1:100,

Date

Drawn B SIFUNA

Checked F WANYONYI